
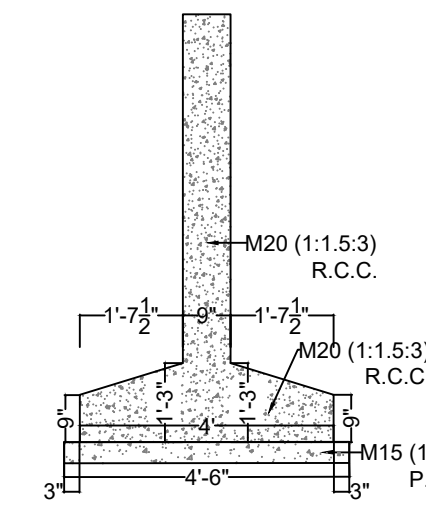
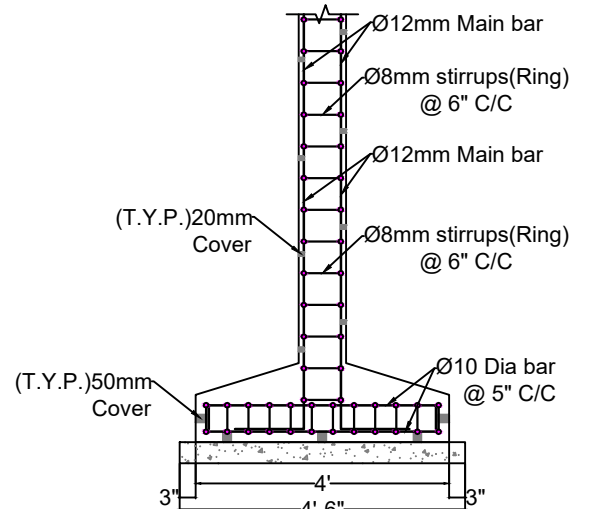
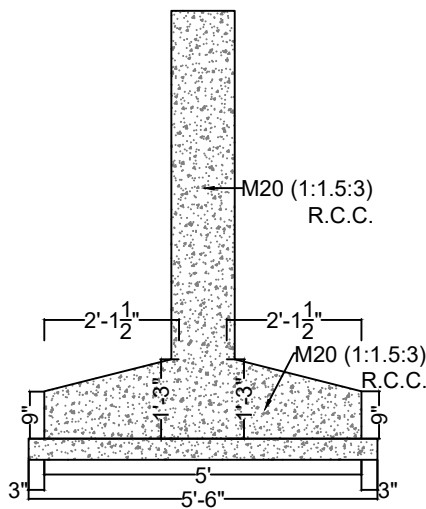
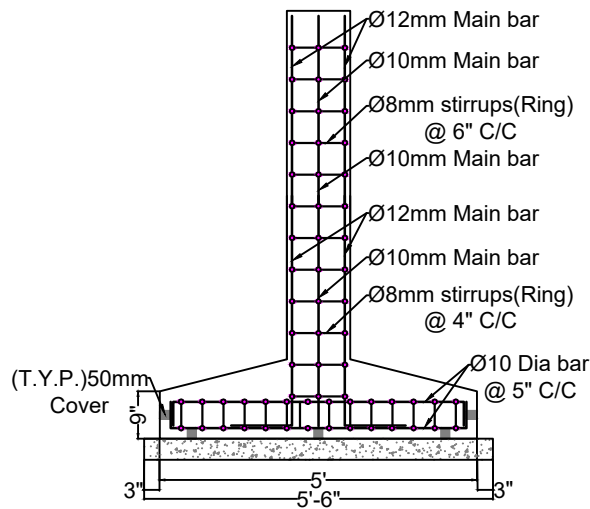
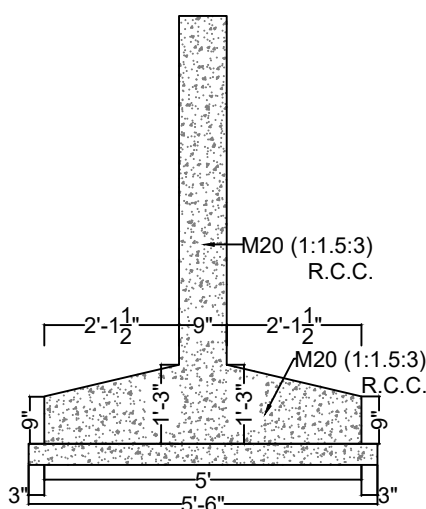
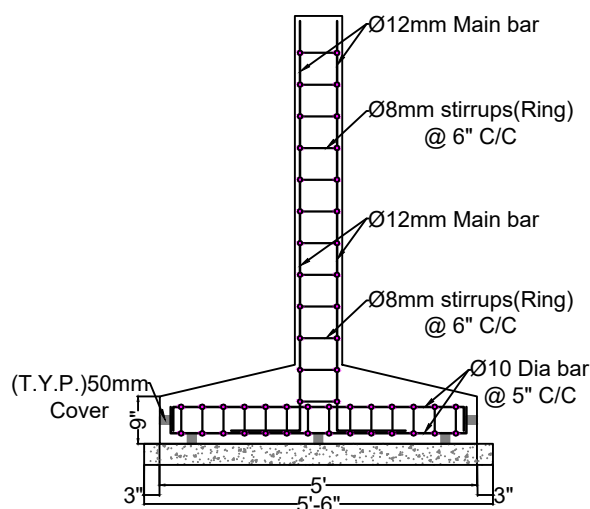
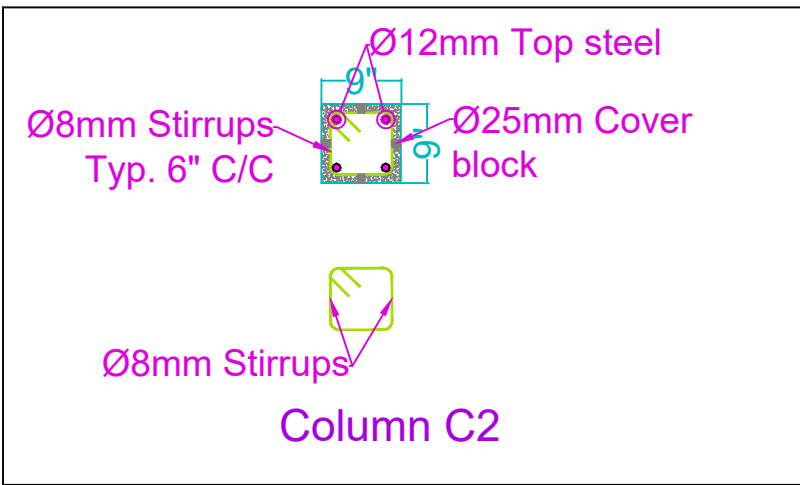
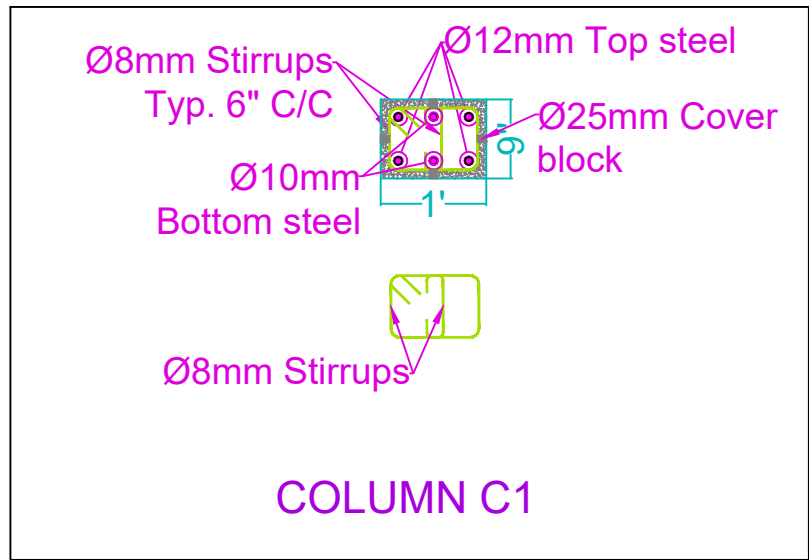


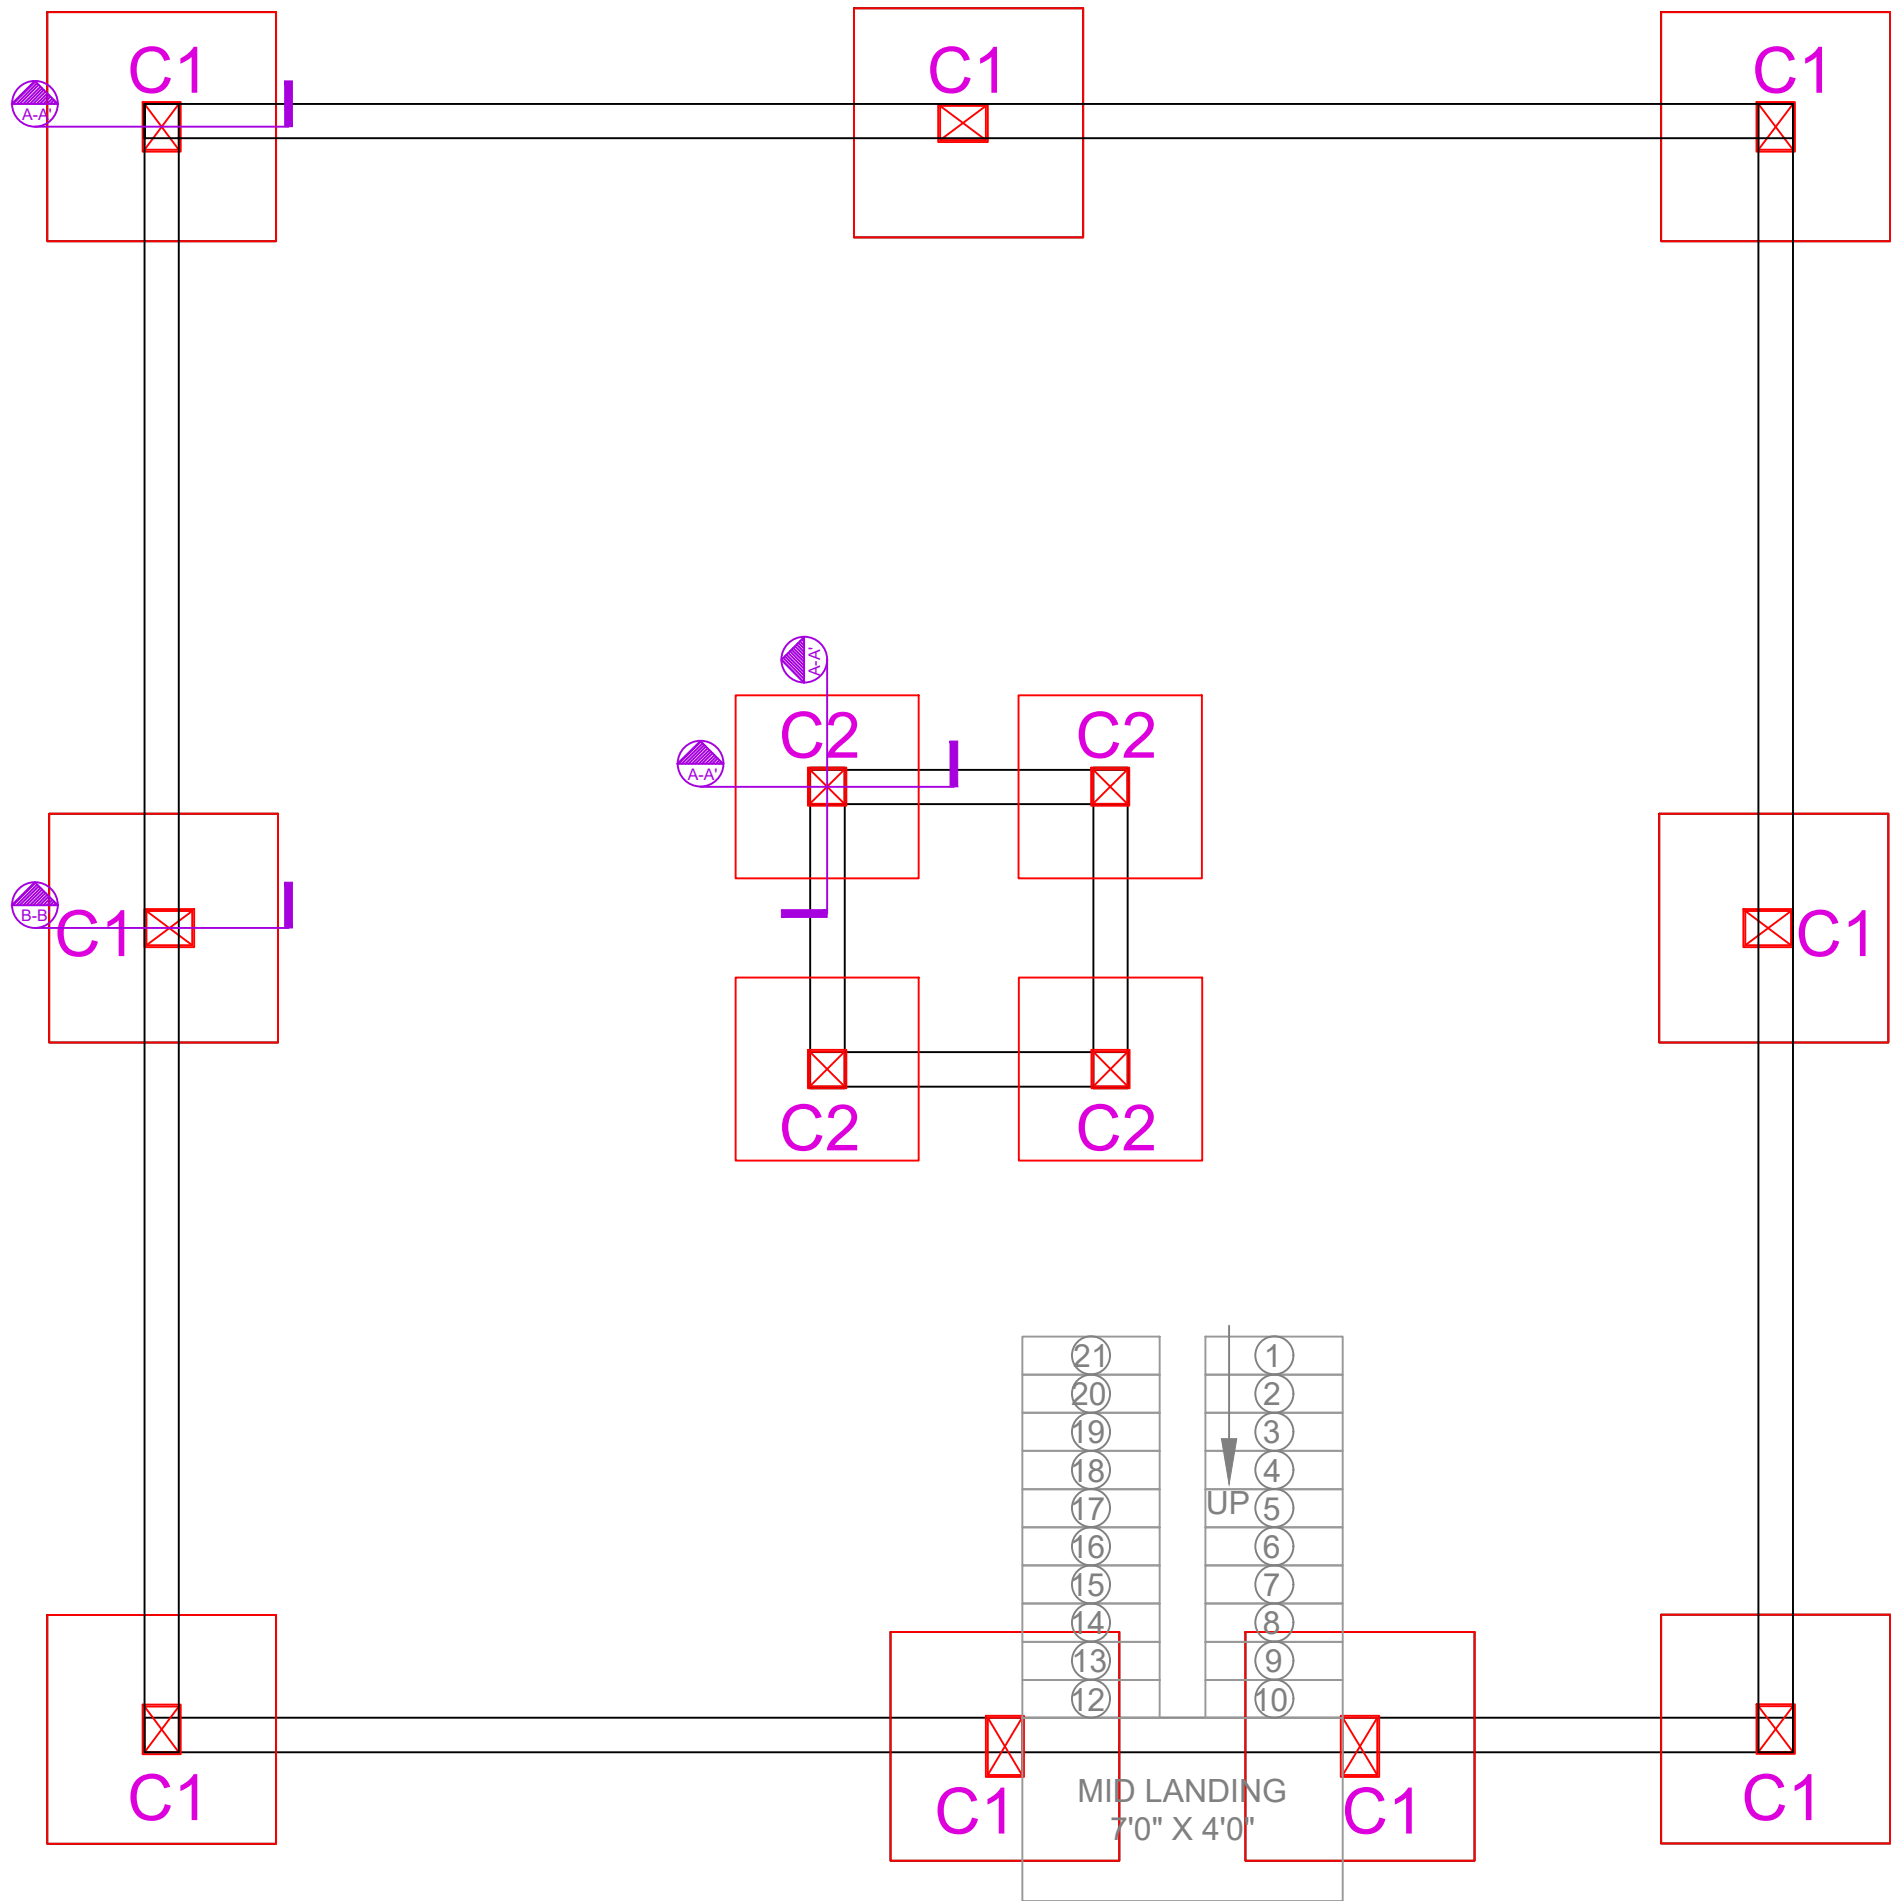

SECTION FOR COLUMN C2 (9"X9")

CLIENT:
Mr. Ripeshbhai Patel

DRAWING TITLE:
FOOTING LAYOUT WITH SECTION

STATUS:
CONCEPT LAYOUT

PROJECT:
RESIDENCE

DATE.:
24.01.2025

DRAWING NO.:
J-102-CV-R0

NOTE:



- 1) All drawings shall be read in construction with relevant Arch. Drg. and any discrepancy shall be brought to notice before start of work.
- 2) Any Drg. shall not be scaled. only written dimensions shall be followed.
- 3) Contractor shall be fully responsible for all temporary works including all R.C.C. work and Brick work.

R.C.C. Notes:

- 1) All concrete shall be of M20 Grade conforming to IS code 450.
- 2) Denotes HYSD bar Fe 500 Grade conforming to IS 1786.
- 3) Reinforcement shall be bent & fixed in accordance with procedure specified in IS 2502.
- 4) Lap length shall be 50 times DIA in mm of bar.
- 5) All footing should be at same level.
- 6) Clear cover to main reinforcements shall be as follows,
- 7) 50 mm for foundation (2 inches)
- 8) 40 mm for columns (1.5 inches)
- 9) 20 mm for beam and slab (1 inch)

SCALE
N.T.S

CHECKED BY
ENG. JAY PATEL

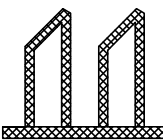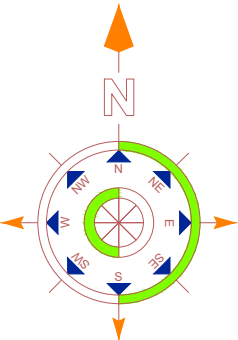

DREAMDESIGN
CIVIL ENGINEER AND
INTERIOR DESIGNERS &
APPROVED VALUER

103,SUKHDDHAM ENCLAVE,
PARIVAR CHAR RASTA,
WAGHODIA DABHOI ROAD,
VADODARA-390025.

PH: +91 6355135078
E-MAIL: jaypatel31032000@gmail.com