

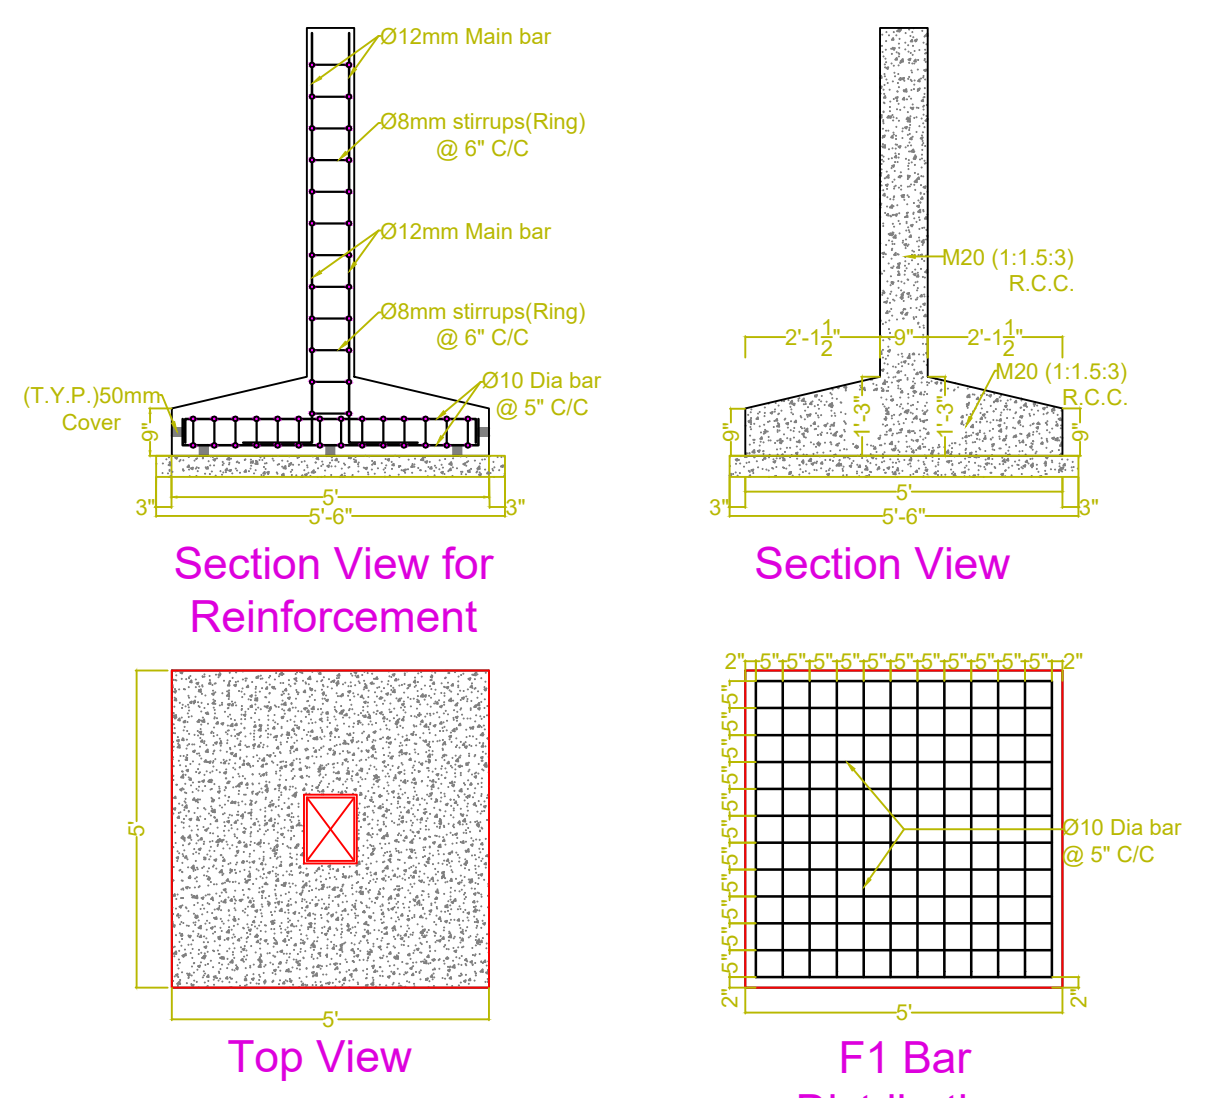


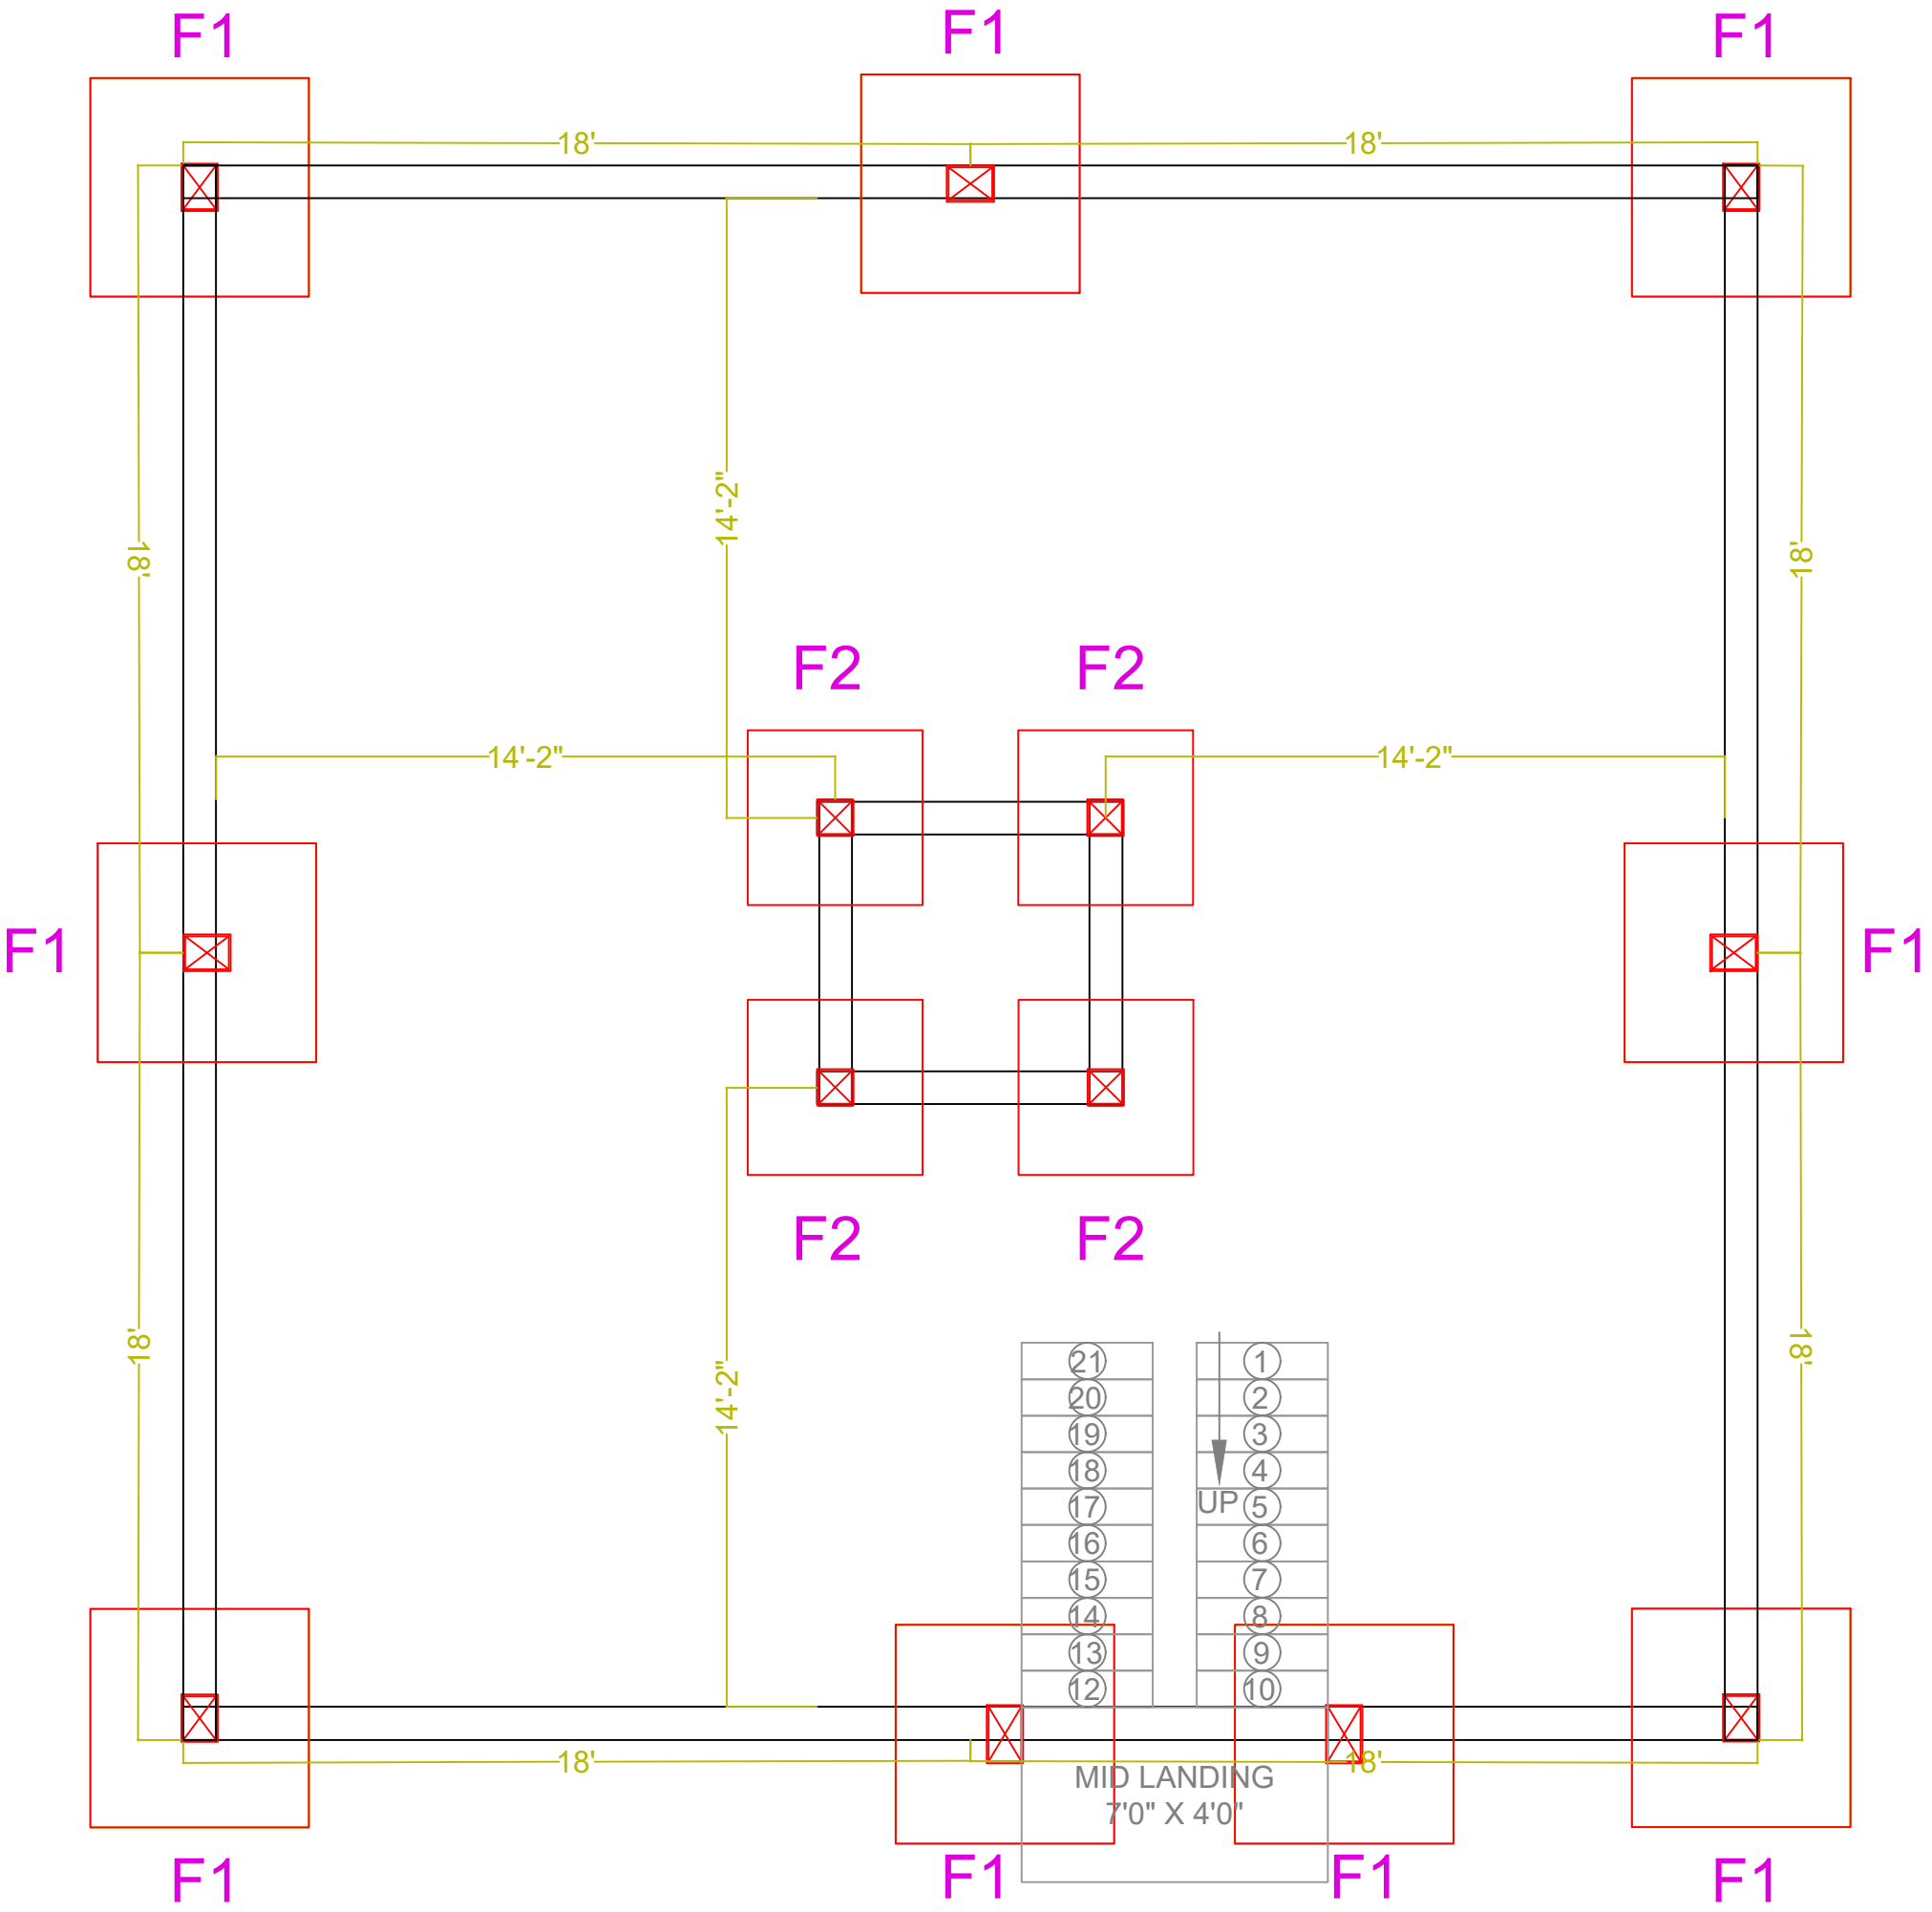

## SECTION FOR FOOTING F1

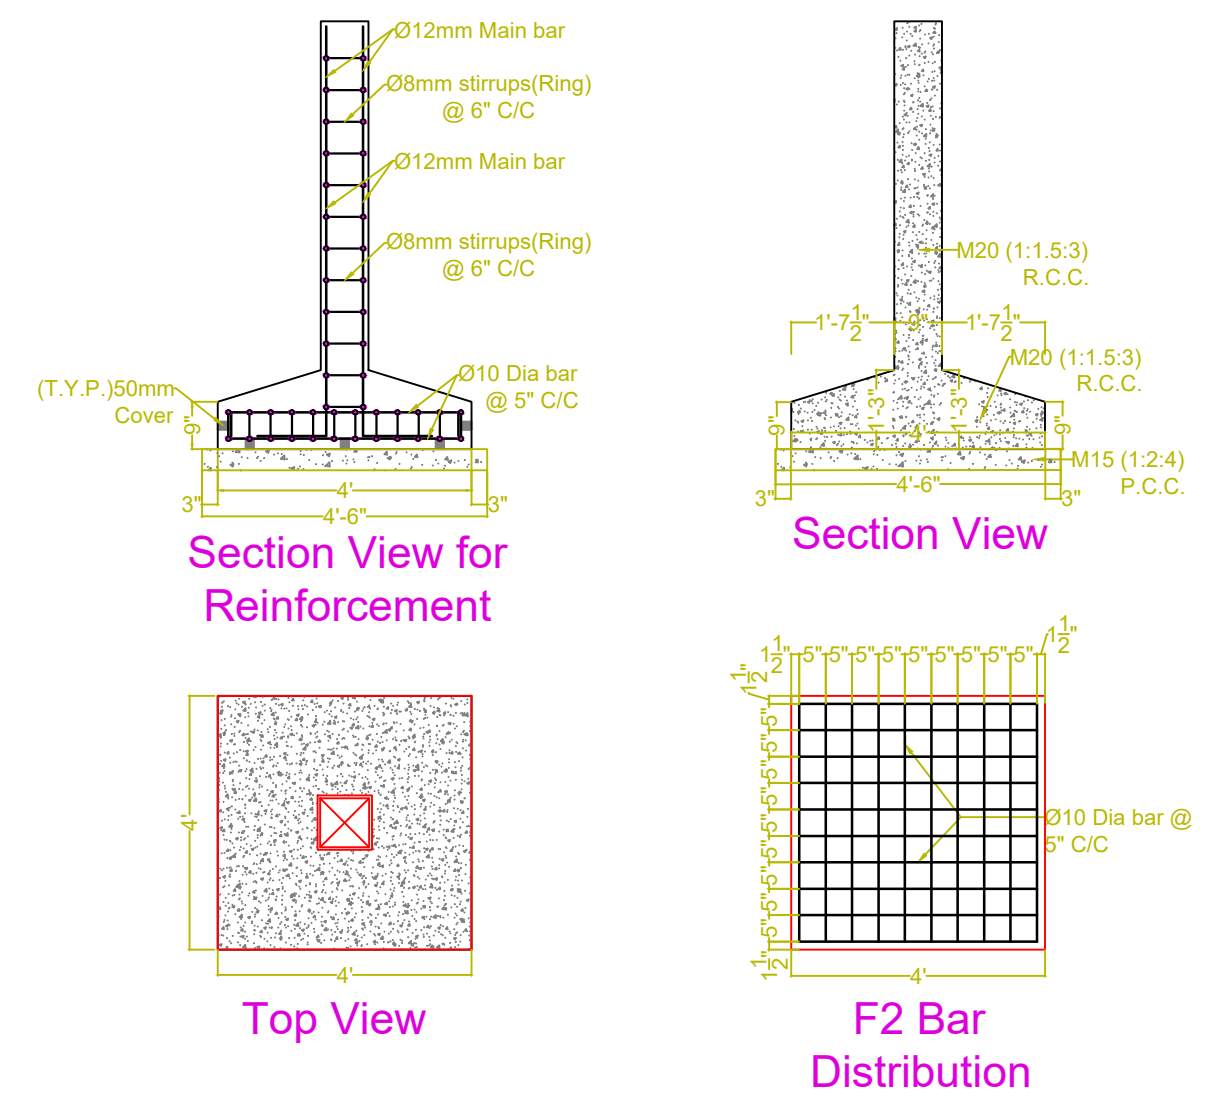

## SECTION FOR FOOTING F2

**CLIENT:**  
Mr. Ripeshbhai Patel

**DRAWING TITLE:**  
FOOTING LAYOUT WITH SECTION

**STATUS:**  
CONCEPT LAYOUT

**PROJECT:**  
RESIDENCE

**DATE.:**  
24.01.2025

**DRAWING NO.:**  
J-102-CV-R0

**NOTE:**  
1) All drawings shall be read in construction with relevant Arch. Drg. and any discrepancy shall be brought to notice before start of work.  
2) Any Drg. shall not be scaled. only written dimensions shall be followed.  
3) Contractor shall be fully responsible for all temporary works including all R.C.C. work and Brick work.

**R.C.C. Notes:**  
1) All concrete shall be of M20 Grade conforming to IS code 450.  
2) Denotes HYSD bar Fe 500 Grade conforming to IS 1786.  
3) Reinforcement shall be bent & fixed in accordance with procedure specified in IS 2502.  
4) Lap length shall be 50 times DIA in mm of bar.  
5) All footing should be at same level.  
6) Clear cover to main reinforcements shall be as follows,  
7) 50 mm for foundation (2 inches)  
8) 40 mm for columns (1.5 inches)  
9) 20 mm for beam and slab (1 inch)

**SCALE**  
N.T.S

**CHECKED BY**  
ENG. JAY PATEL

**DREAMDESIGN**  
CIVIL ENGINEER AND  
INTERIOR DESIGNERS &  
APPROVED VALUER

103,SUKHDDHAM ENCLAVE,  
PARIVAR CHAR RASTA,  
WAGHODIA DABHOI ROAD,  
VADODARA-390025.

PH: +91 6355135078  
E-MAIL: jaypatel31032000@gmail.com