
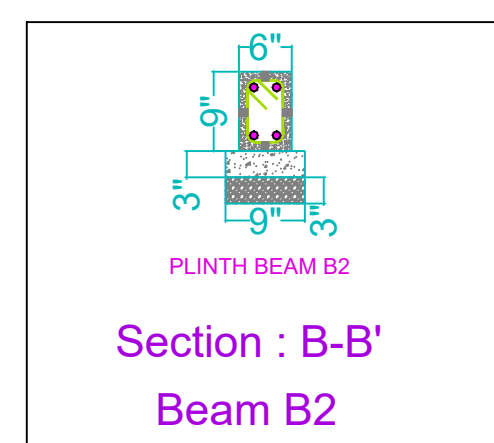
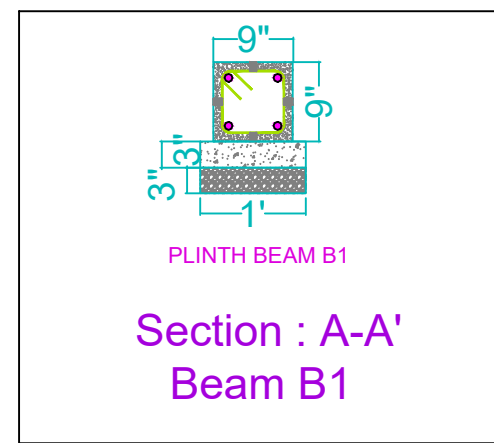
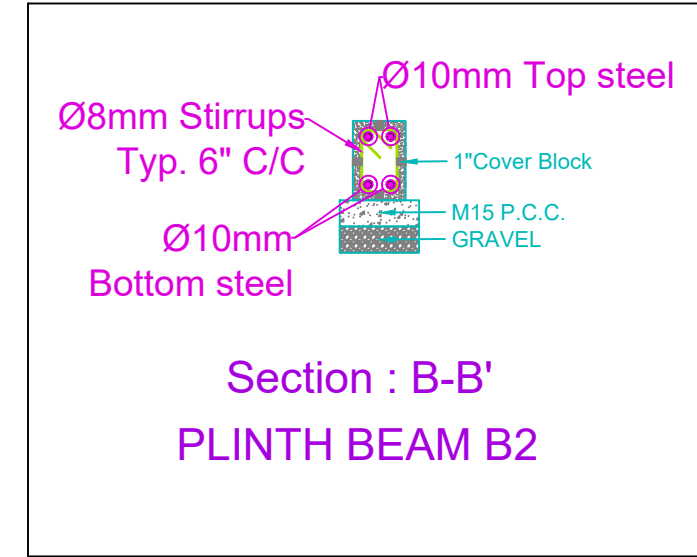
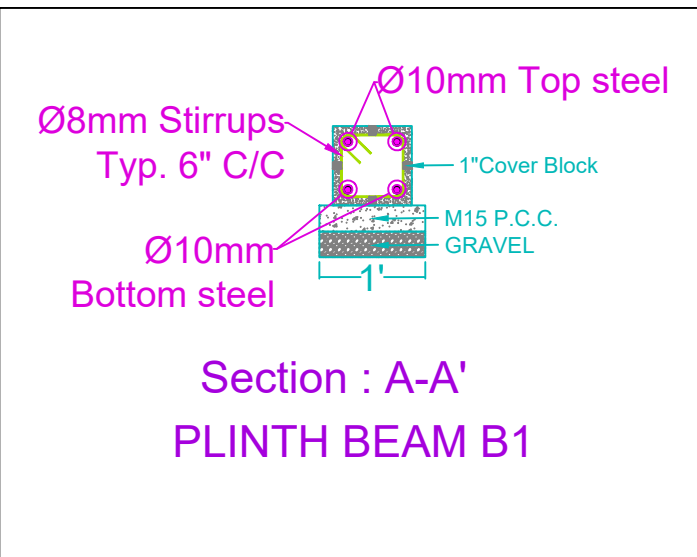
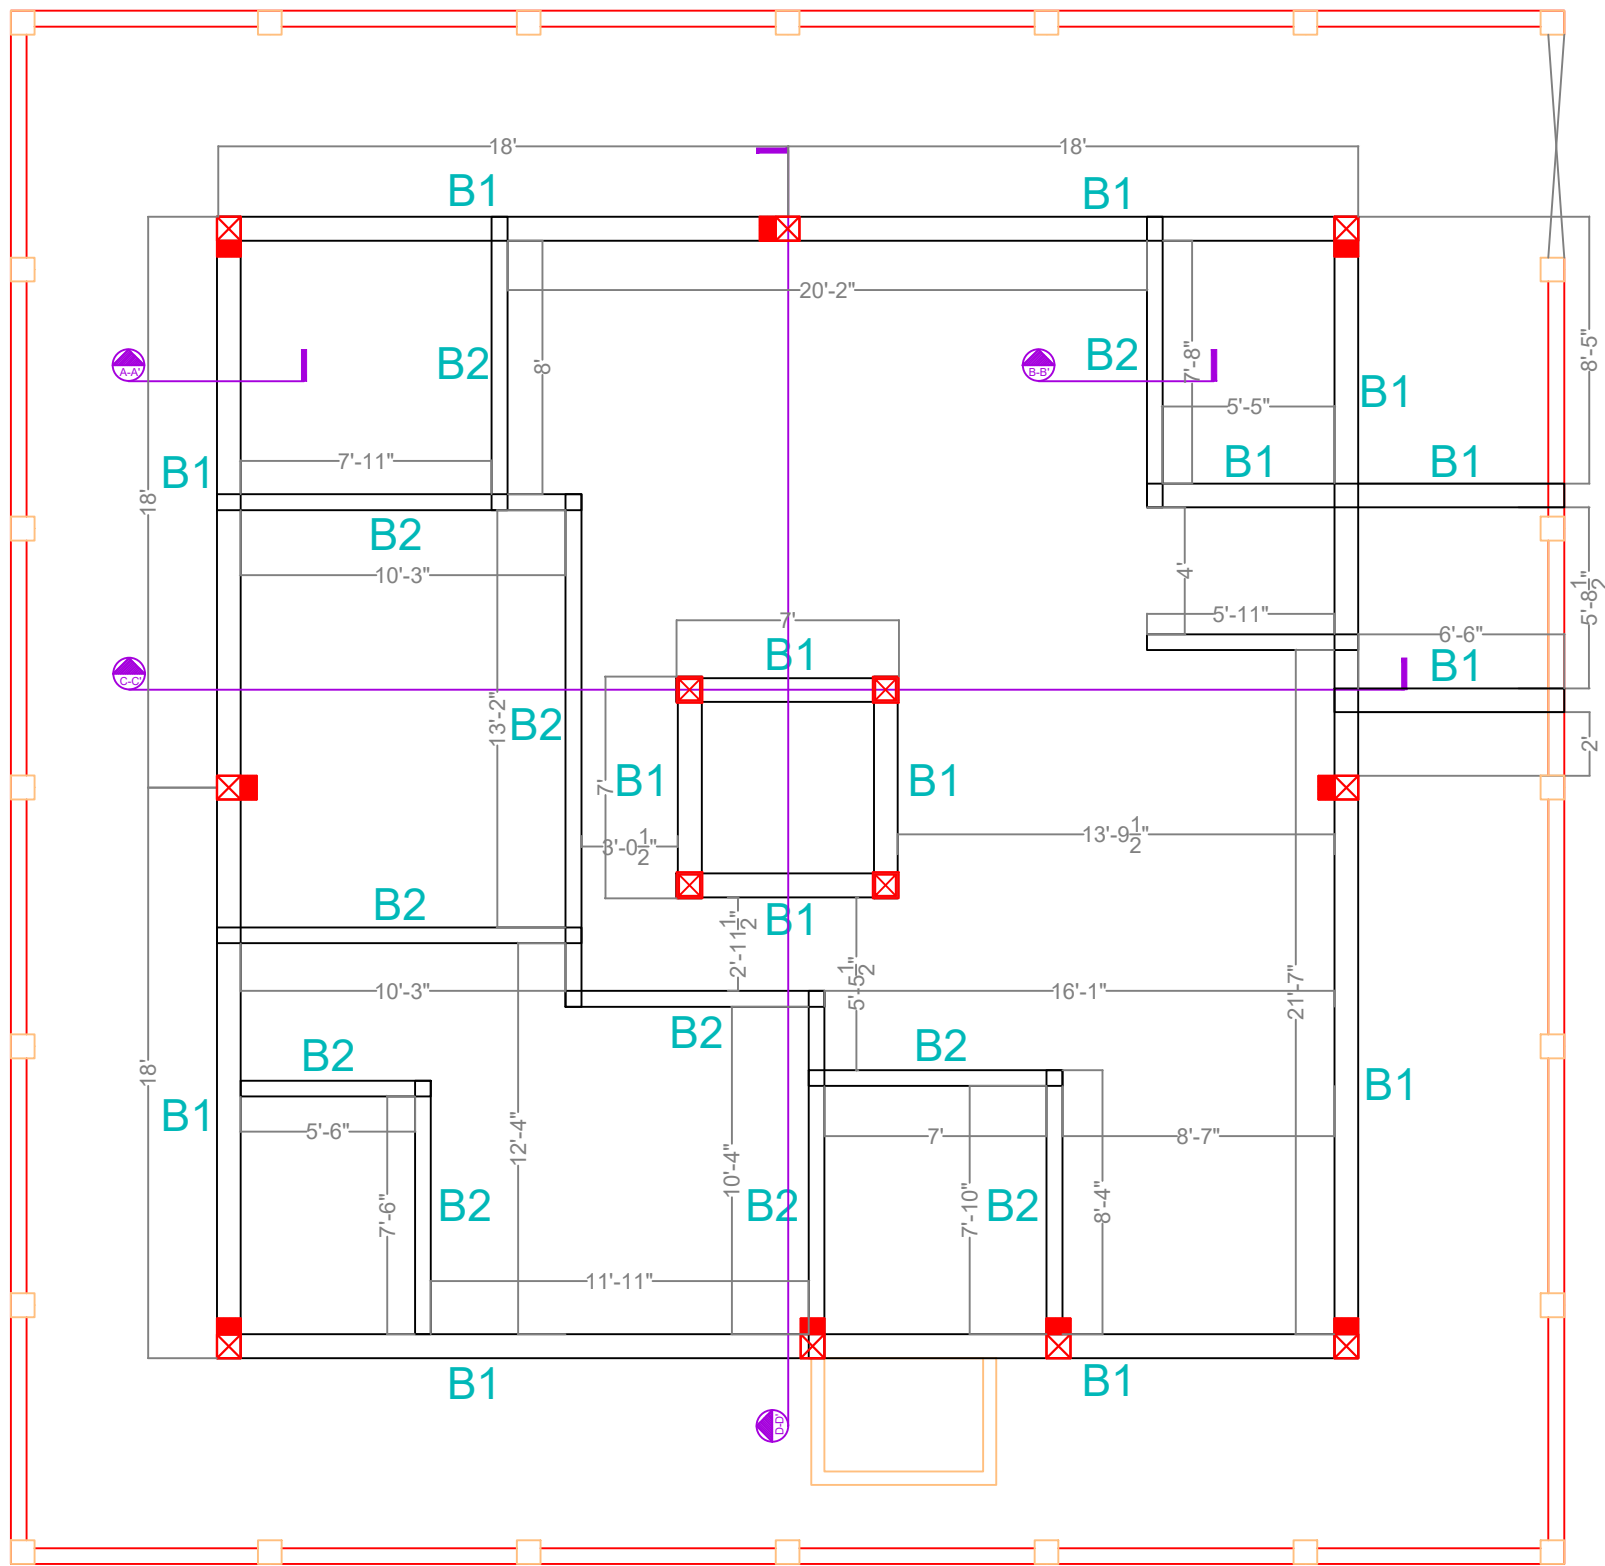


Section : C-C'

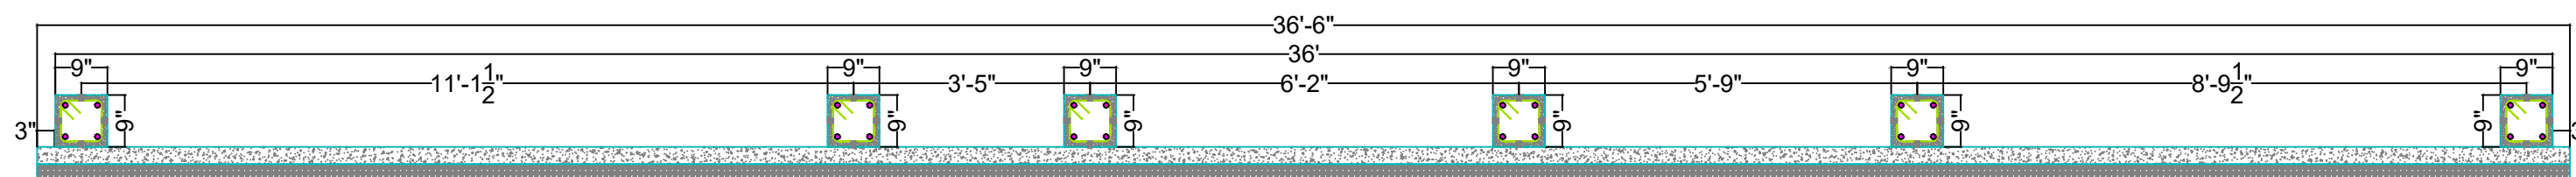

Section : D-D'

CLIENT:
Mr. Ripeshbhai Patel

DRAWING TITLE:
GROUND FLOOR PLINTH BEAM LAYOUT & SECTION

STATUS:
CONCEPT LAYOUT

PROJECT:
RESIDENCE

DATE.:
09.03.2025

DRAWING NO.:
J-102-CV-R1

SCALE
N.T.S

CHECKED BY
ENG. JAY PATEL

NOTE:

1. This drawing is the property of DREAM DESIGN and not to be copied or used without permission.
2. All dimensions are to be read and not to be measured.
3. DREAM DESIGN must be informed if any discrepancies, lack of information in drawing or in case of any required alternations executions of work.

DREAMDESIGN
CIVIL ENGINEER AND
INTERIOR DESIGNERS &
APPROVED VALUER

103,SUKHDDHAM ENCLAVE,
PARIVAR CHAR RASTA,
WAGHODIA DABHOI ROAD,
VADODARA-390025.

PH: +91 6355135078
E-MAIL: jaypatel31032000@.com

