
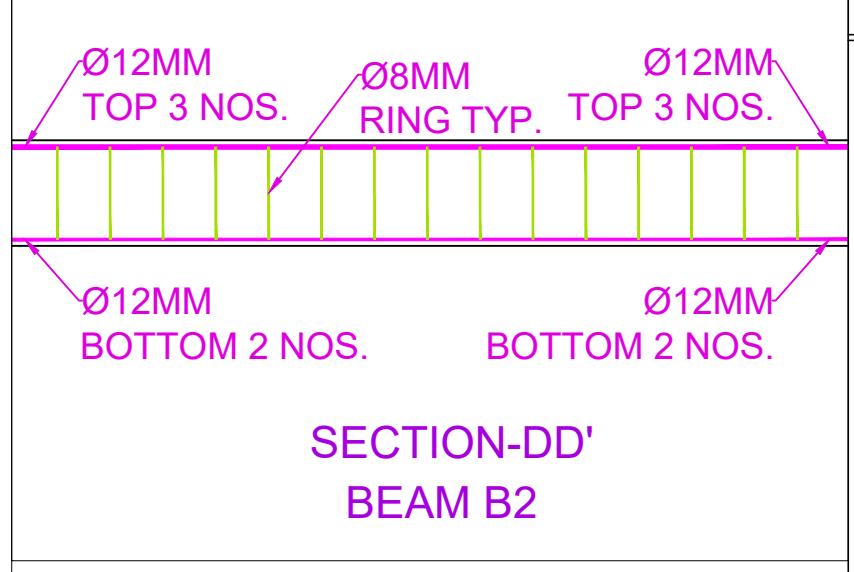
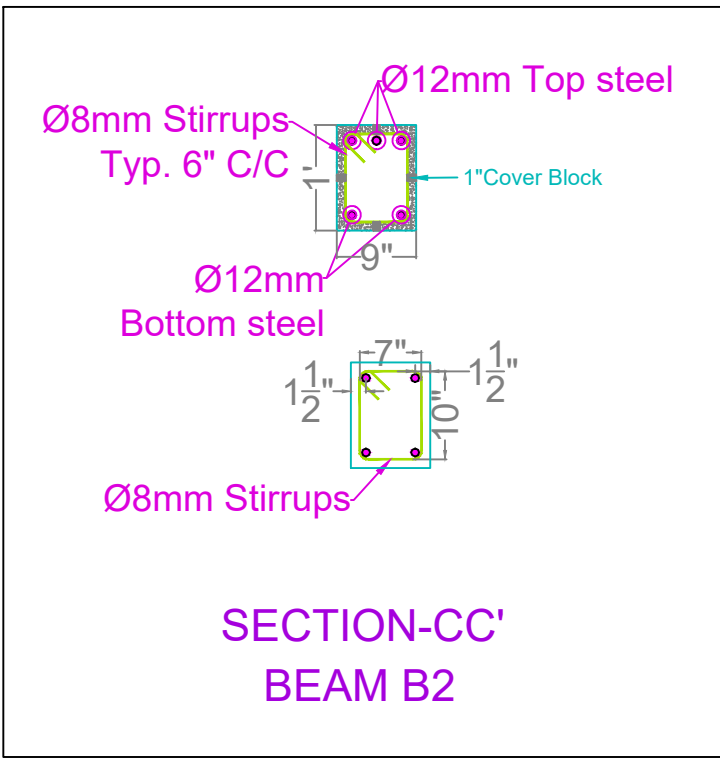
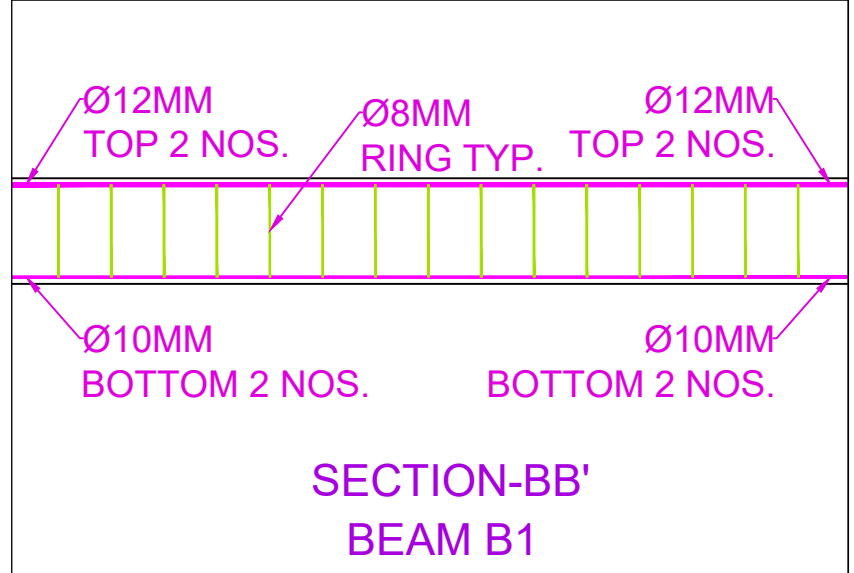
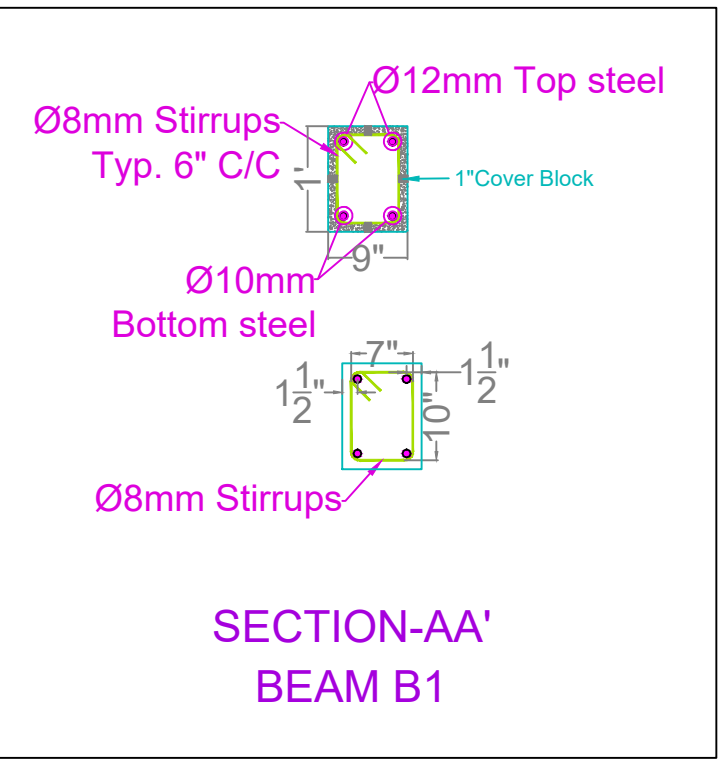


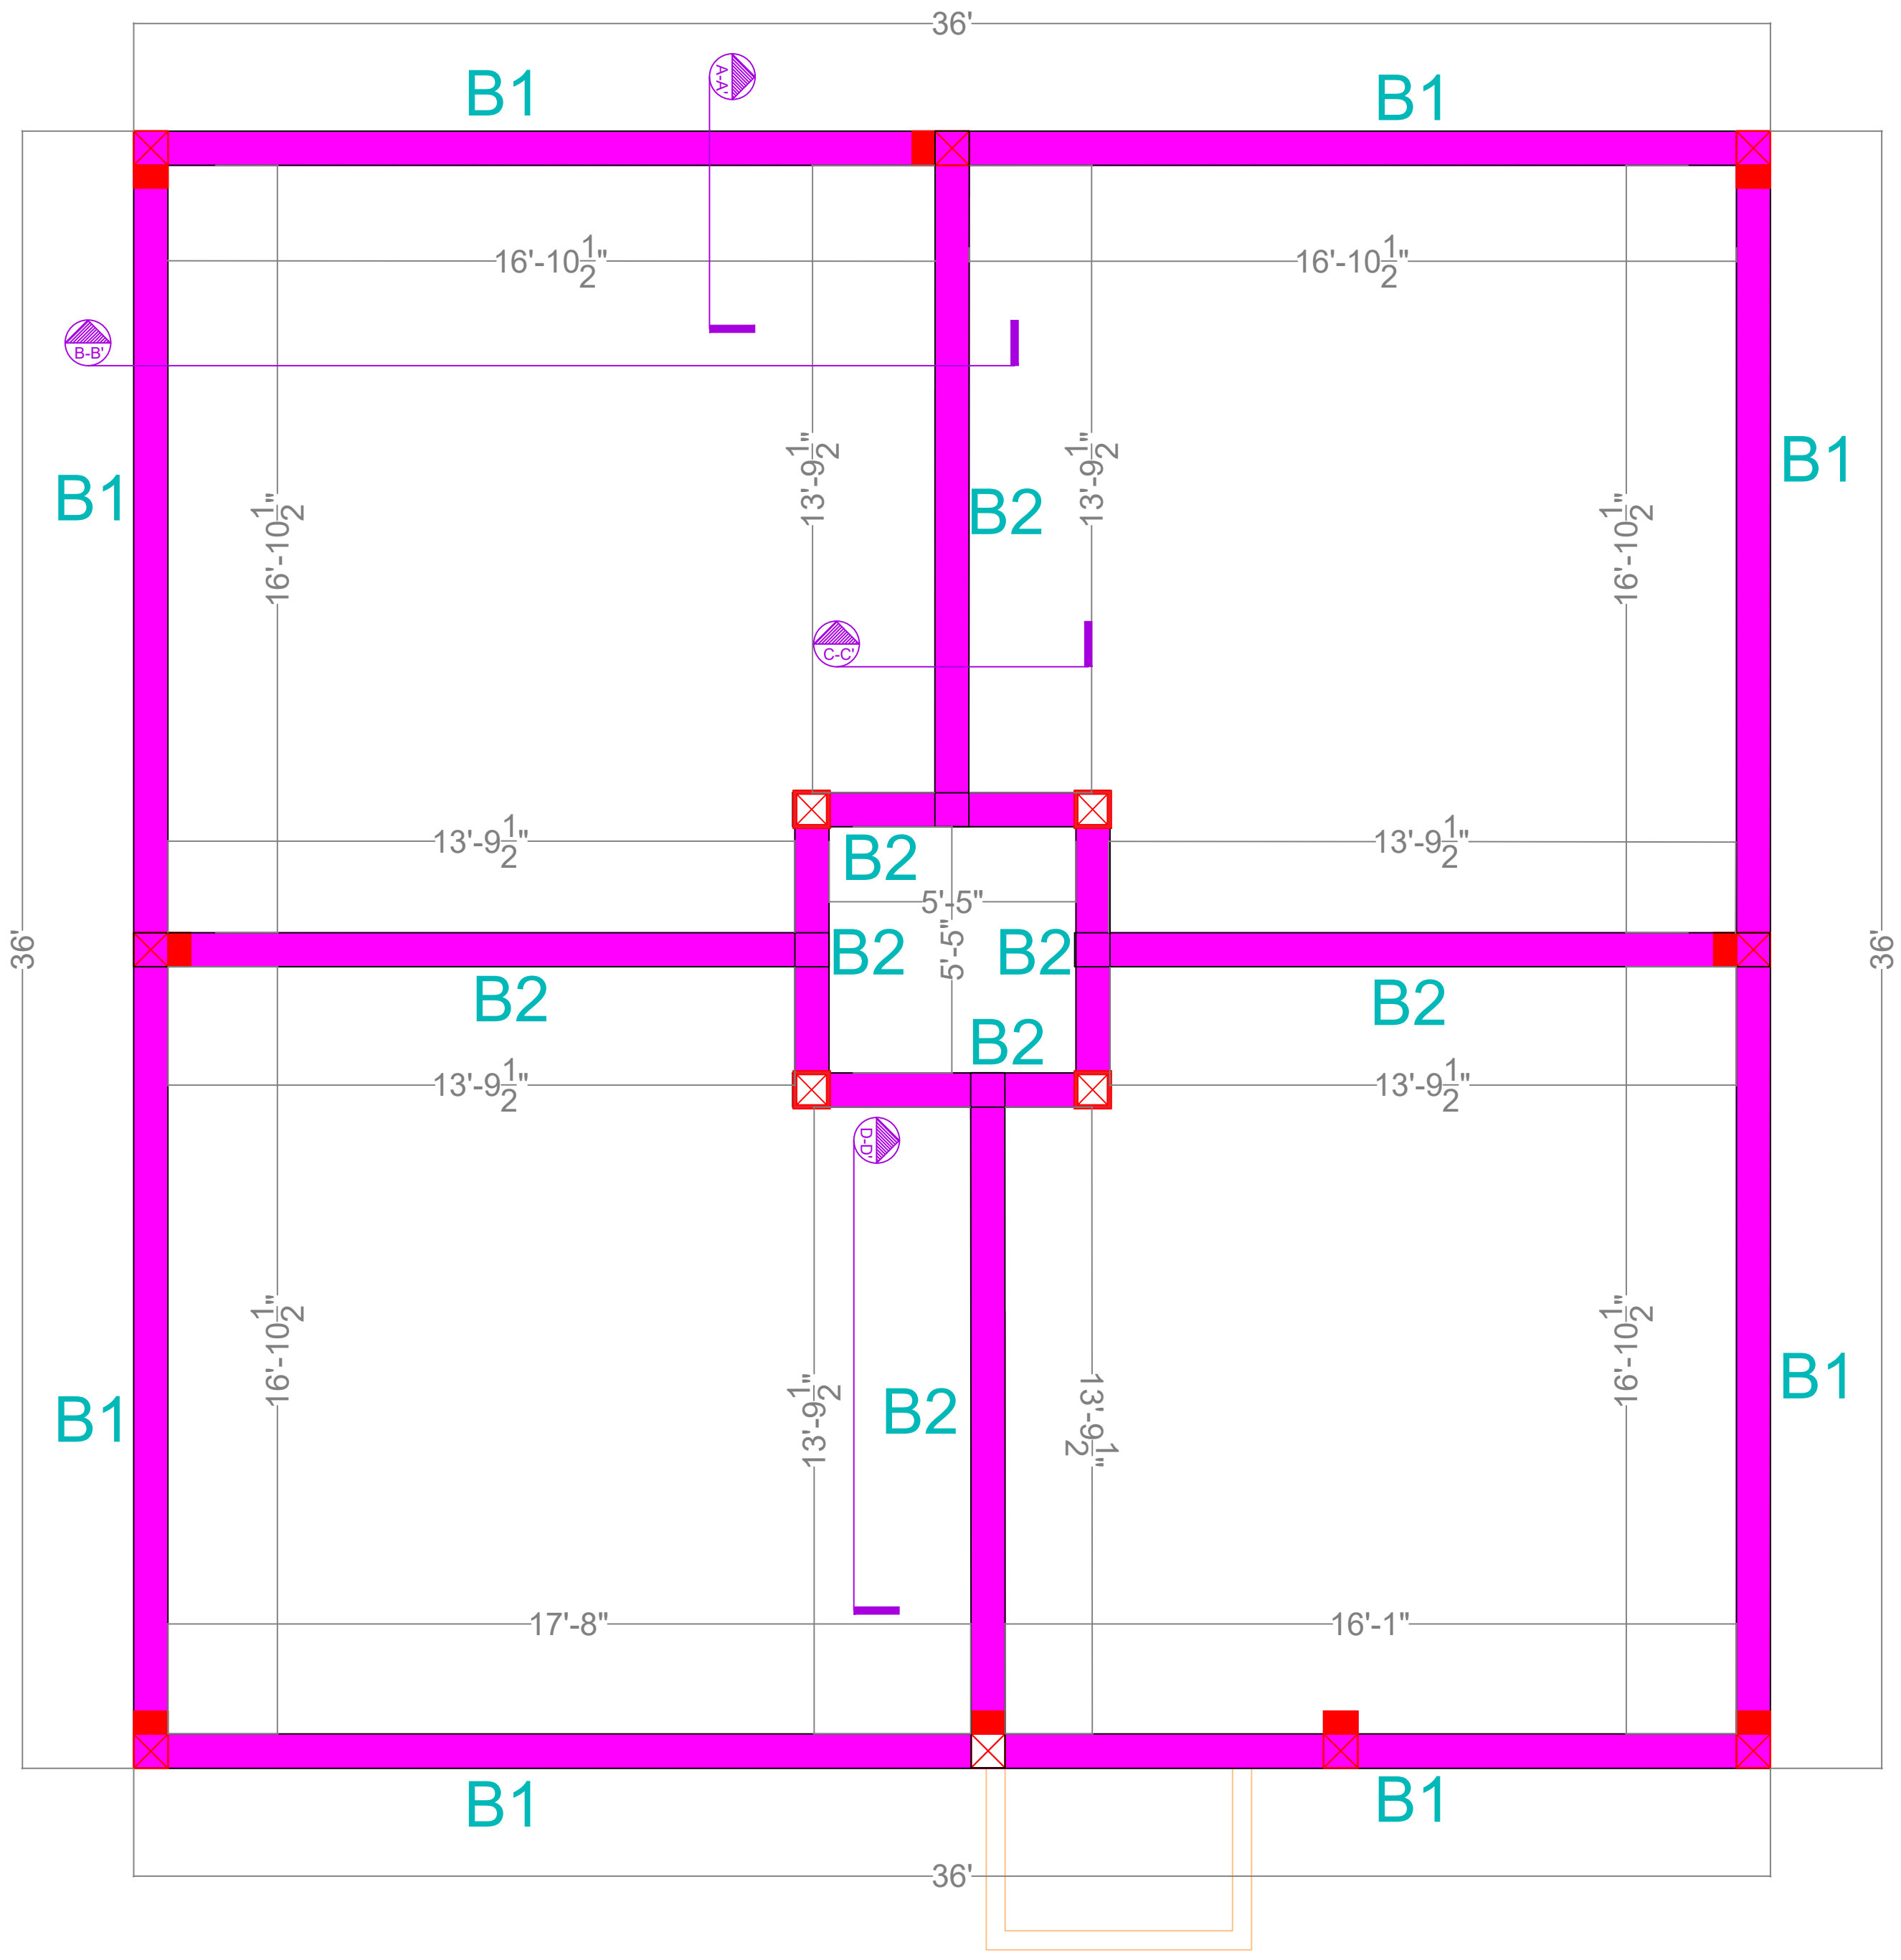

CLIENT: Mr. Ripeshbhai Patel	
DRAWING TITLE: GROUND FLOOR SLAB BEAM LAYOUT & SECTION	
STATUS: SLAB BEAM DETAIL LAYOUT	
PROJECT: RESIDENCE	
DATE.: 03.07.2025	DRAWING NO.: J-102-CV-R1

SCALE
N.T.S

CHECKED BY
ENG. JAY PATEL

NOTE:

1. This drawing is the property of DREAM DESIGN and not to be copied or used without permission.
2. All dimensions are to be read and not to be measured.
3. DREAM DESIGN must be informed if any discrepancies, lack of information in drawing or in case of any required alternations executions of work.

DREAMDESIGN
CIVIL ENGINEER AND
INTERIOR DESIGNERS &
APPROVED VALUER

103,SUKHDDHAM ENCLAVE,
PARIVAR CHAR RASTA,
WAGHODIA DABHOI ROAD,
VADODARA-390025.

PH: +91 6355135078
E-MAIL: jaypatel31032000@gmail.com