


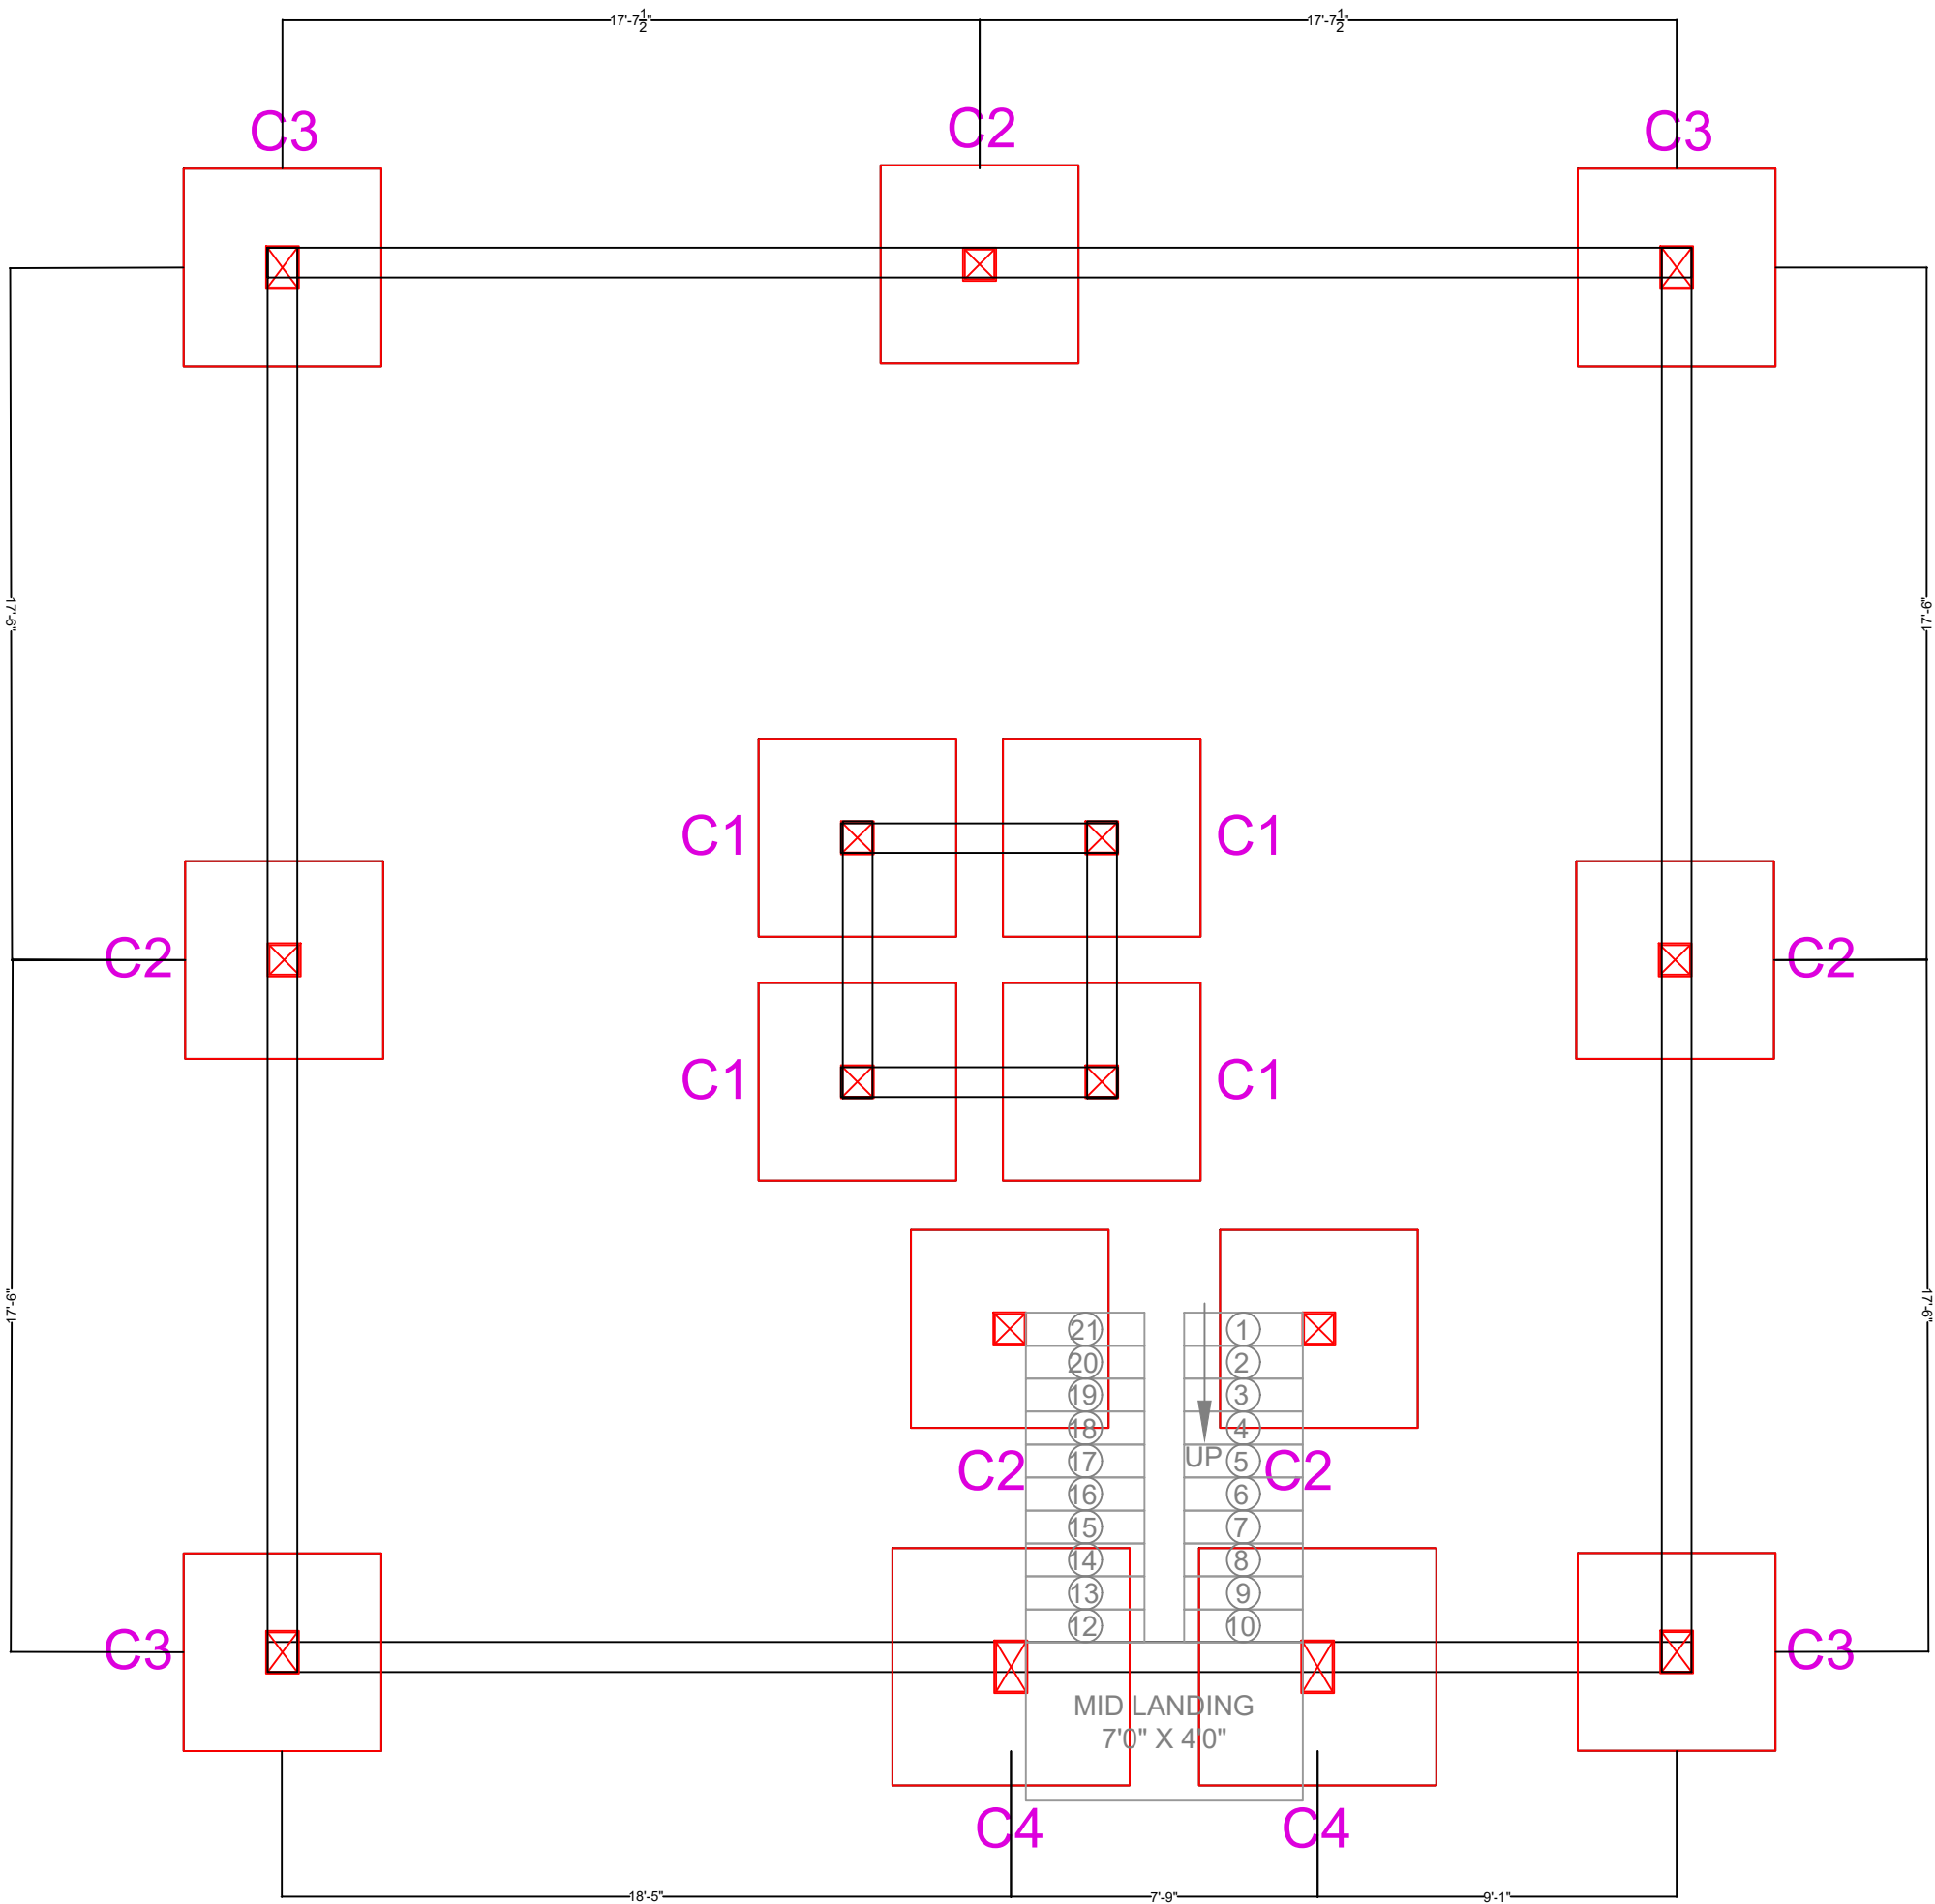

CLIENT:
Mr. Ripeshbhai Patel

DRAWING TITLE:
GROUND FLOOR LAYOUT

STATUS:
CONCEPT LAYOUT

PROJECT:
RESIDENCE

DATE.:
24.11.2024

DRAWING NO.:
J-102-AR-R2

SCHEDULE OF OPENING

DOOR	D1	4'0" X 7'0"
	D2	3'0" X 7'0"
	D3	2'6" X 7'0"
WINDOW	W1	5'0" X 5'0"
	W2	3'0" X 5'0"
	SW	6'0" X 5'0"
VENTILATION	V	1'6" X 1'6"

ENTRANCE STEPS:

- TREAD-12'-0"

- RISER-6"

STAIRCASE STEPS:

- TREAD-10"

- RISER-6"


- CLEAR FLOOR HEIGHT- 11'-0"

- SILL- 3'-0"

- LINTEL-8'-0"

SCALE
N.T.S

CHECKED BY
ENG. JAY PATEL

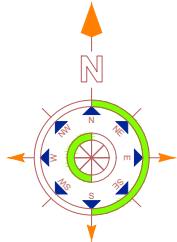

NOTE:

1. This drawing is the property of DREAM DESIGN and not to be copied or used without permission.

2. All dimensions are to be read and not to be measured.

3. DREAM DESIGN must be informed if any discrepancies, lack of information in drawing or in case of any required alternations executions of work.



DREAMDESIGN
CIVIL ENGINEER AND
INTERIOR DESIGNERS &
APPROVED VALUER

103,SUKHDHAM ENCLAVE,
PARIVAR CHAR RASTA,
WAGHODIA DABHOI ROAD,
VADODARA-390025.

PH: +91 6355135078
E-MAIL: jaypatel31032000@gmail.com