


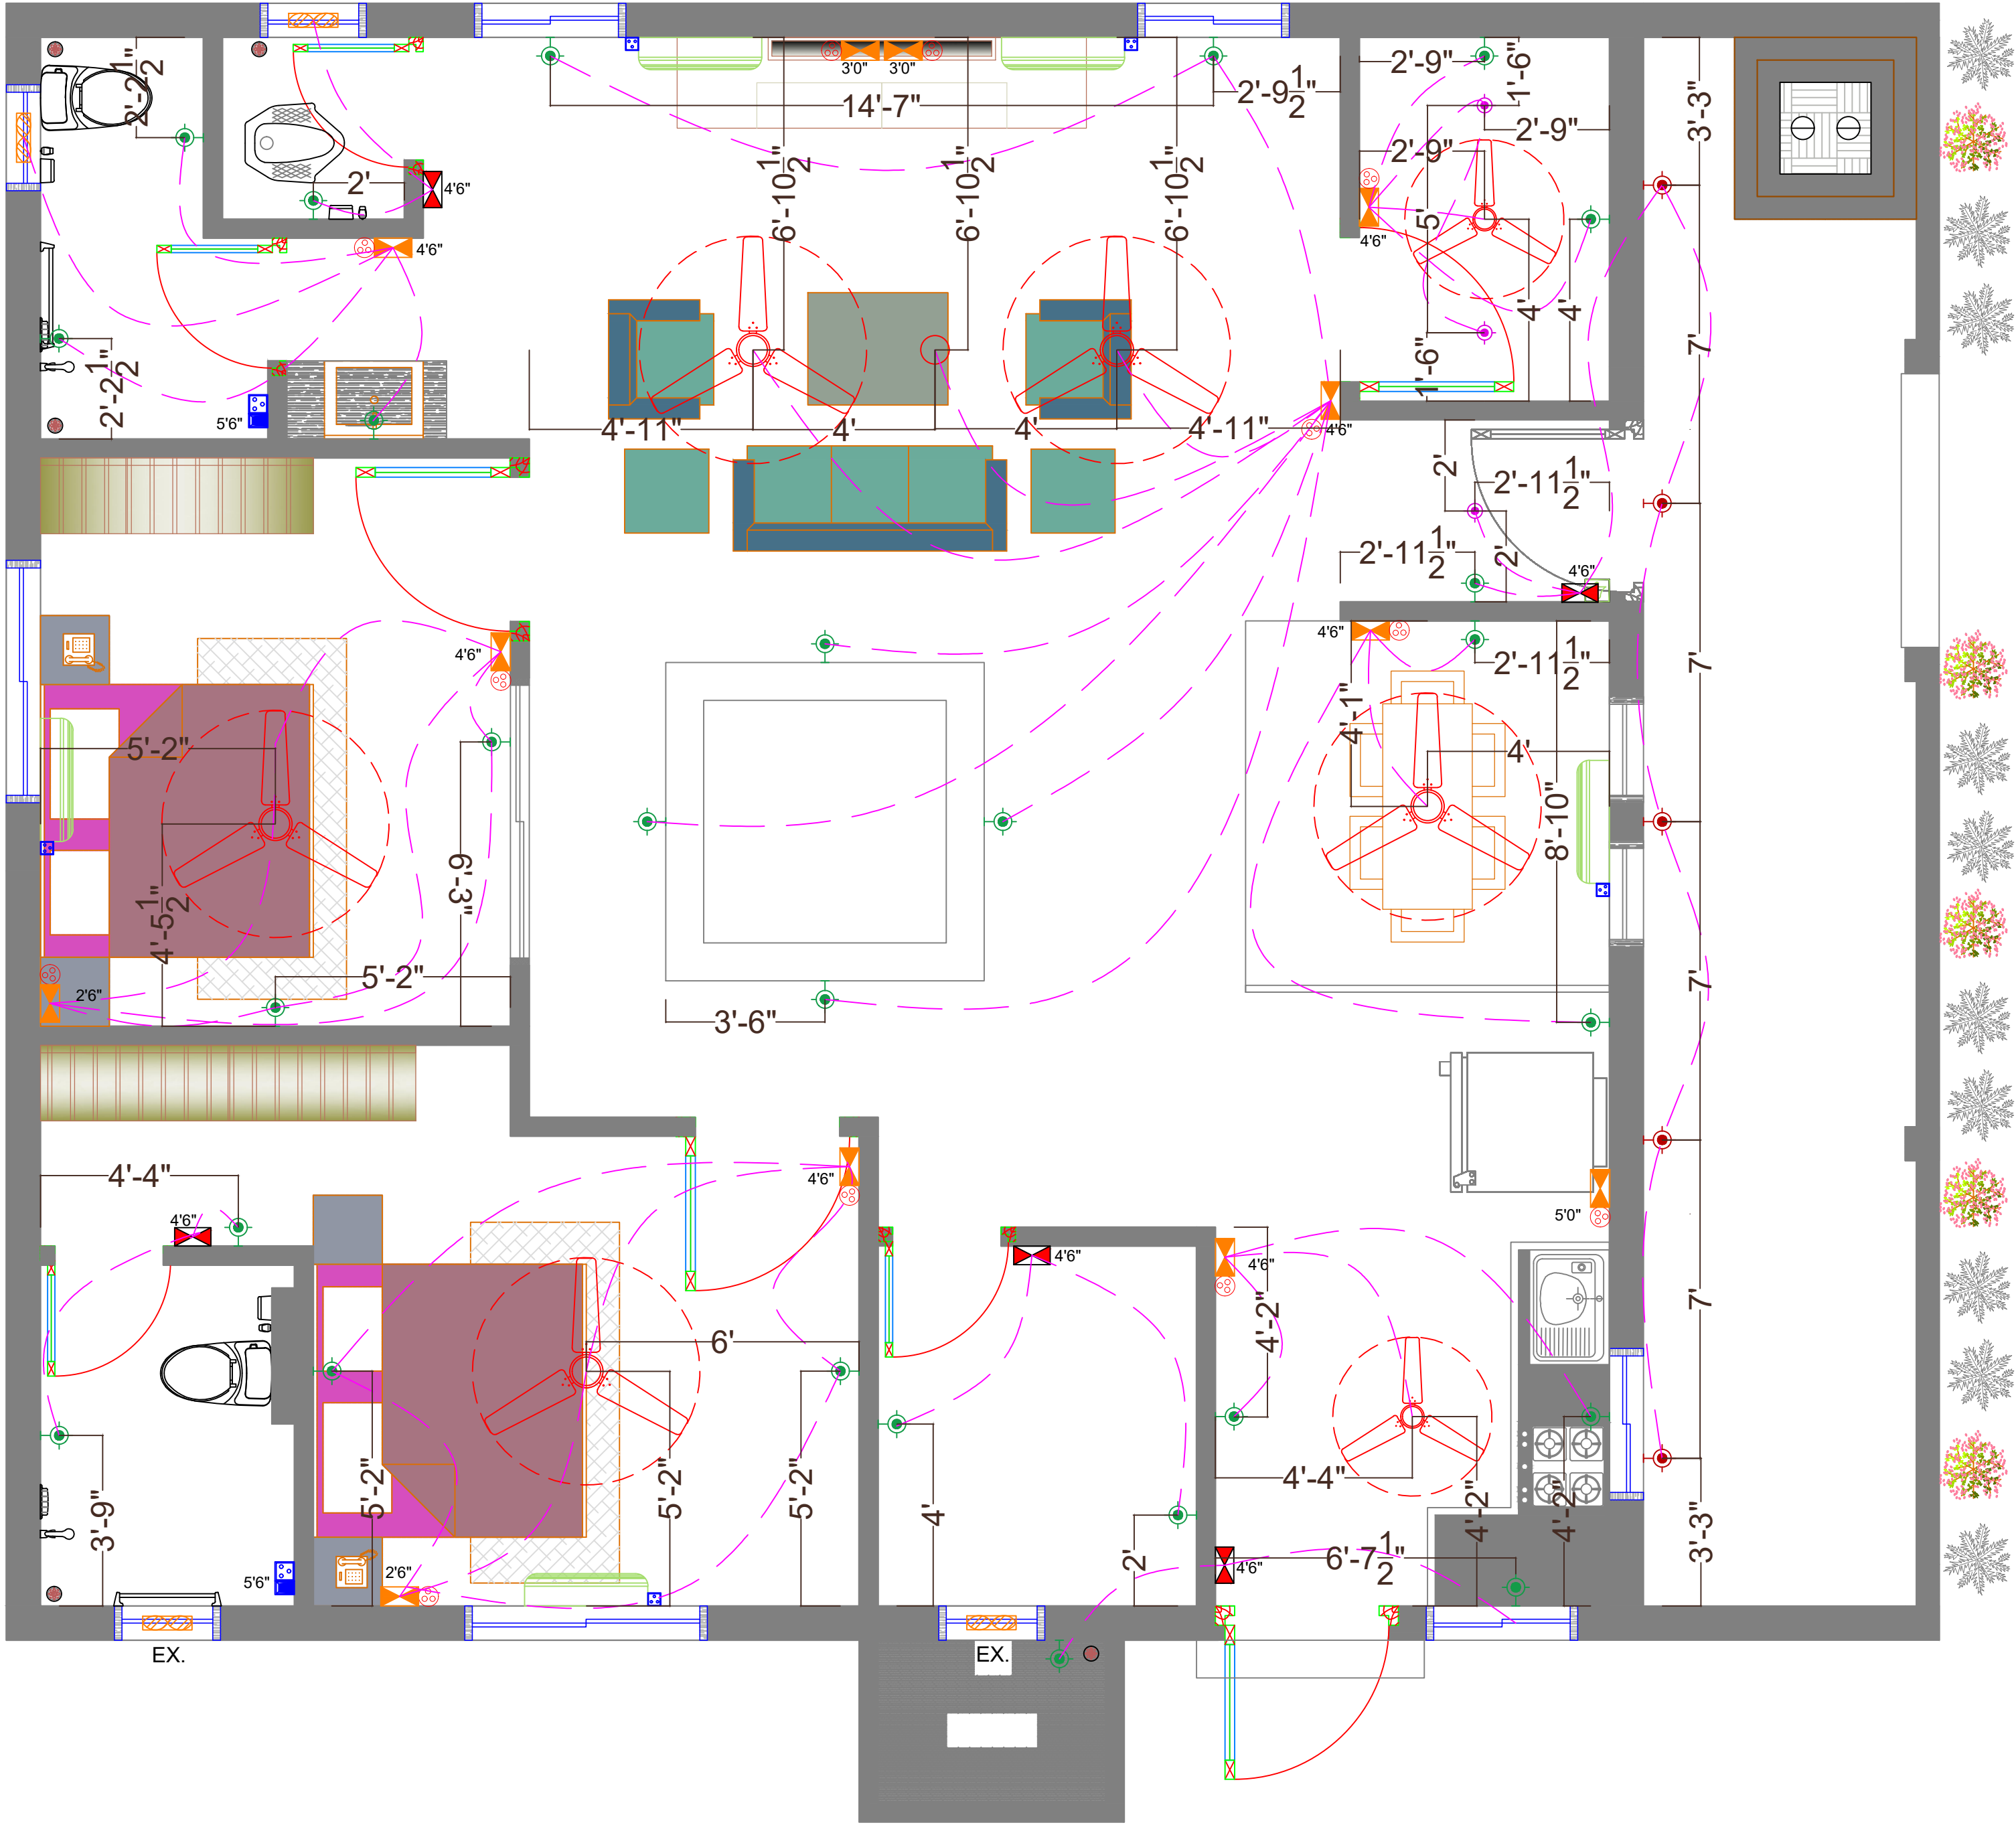

CLIENT:
Mr. Ripeshbhai Patel

DRAWING TITLE:
GROUND FLOOR LAYOUT


STATUS:
ELECTRICAL DRAWING

PROJECT:
RESIDENCE

DATE.:
10.06.2025

DRAWING NO.:
J-102-EL-R1

	SWITCHBOARD
	SWITCH SOCKET BOARD
	5 AMP PLUG POINT
	BRACKET LIGHT
	CEILING LIGHT
	WALL LIGHT
	FAN POINT
	DISTRIBUTION BOX
	METER BOX
	BELL POINT
	COMPOUND WALL LIGHT
	AIR CONDITION
	AC OUTDOOR UNIT
	GEYSER POINT
	EXHAUST FAN

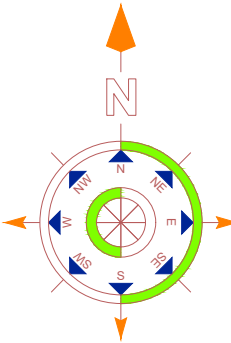


CHECKED BY
ENG. JAY PATEL

SCALE
N.T.S

NOTE:

1. This drawing is the property of DREAM DESIGN and not to be copied or used without permission.
2. All dimensions are to be read and not to be measured.
3. DREAM DESIGN must be informed if any discrepancies, lack of information in drawing or in case of any required alternations executions of work.

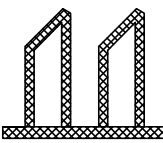

DREAMDESIGN
CIVIL ENGINEER AND
INTERIOR DESIGNERS

103,SUKHDHAM ENCLAVE,
PARIVAR CHAR RASTA,
WAGHODIA DABHOI ROAD,
VADODARA-390025.

PH: +91 6355135078
E-MAIL: jaypatel31032000@gmail.com